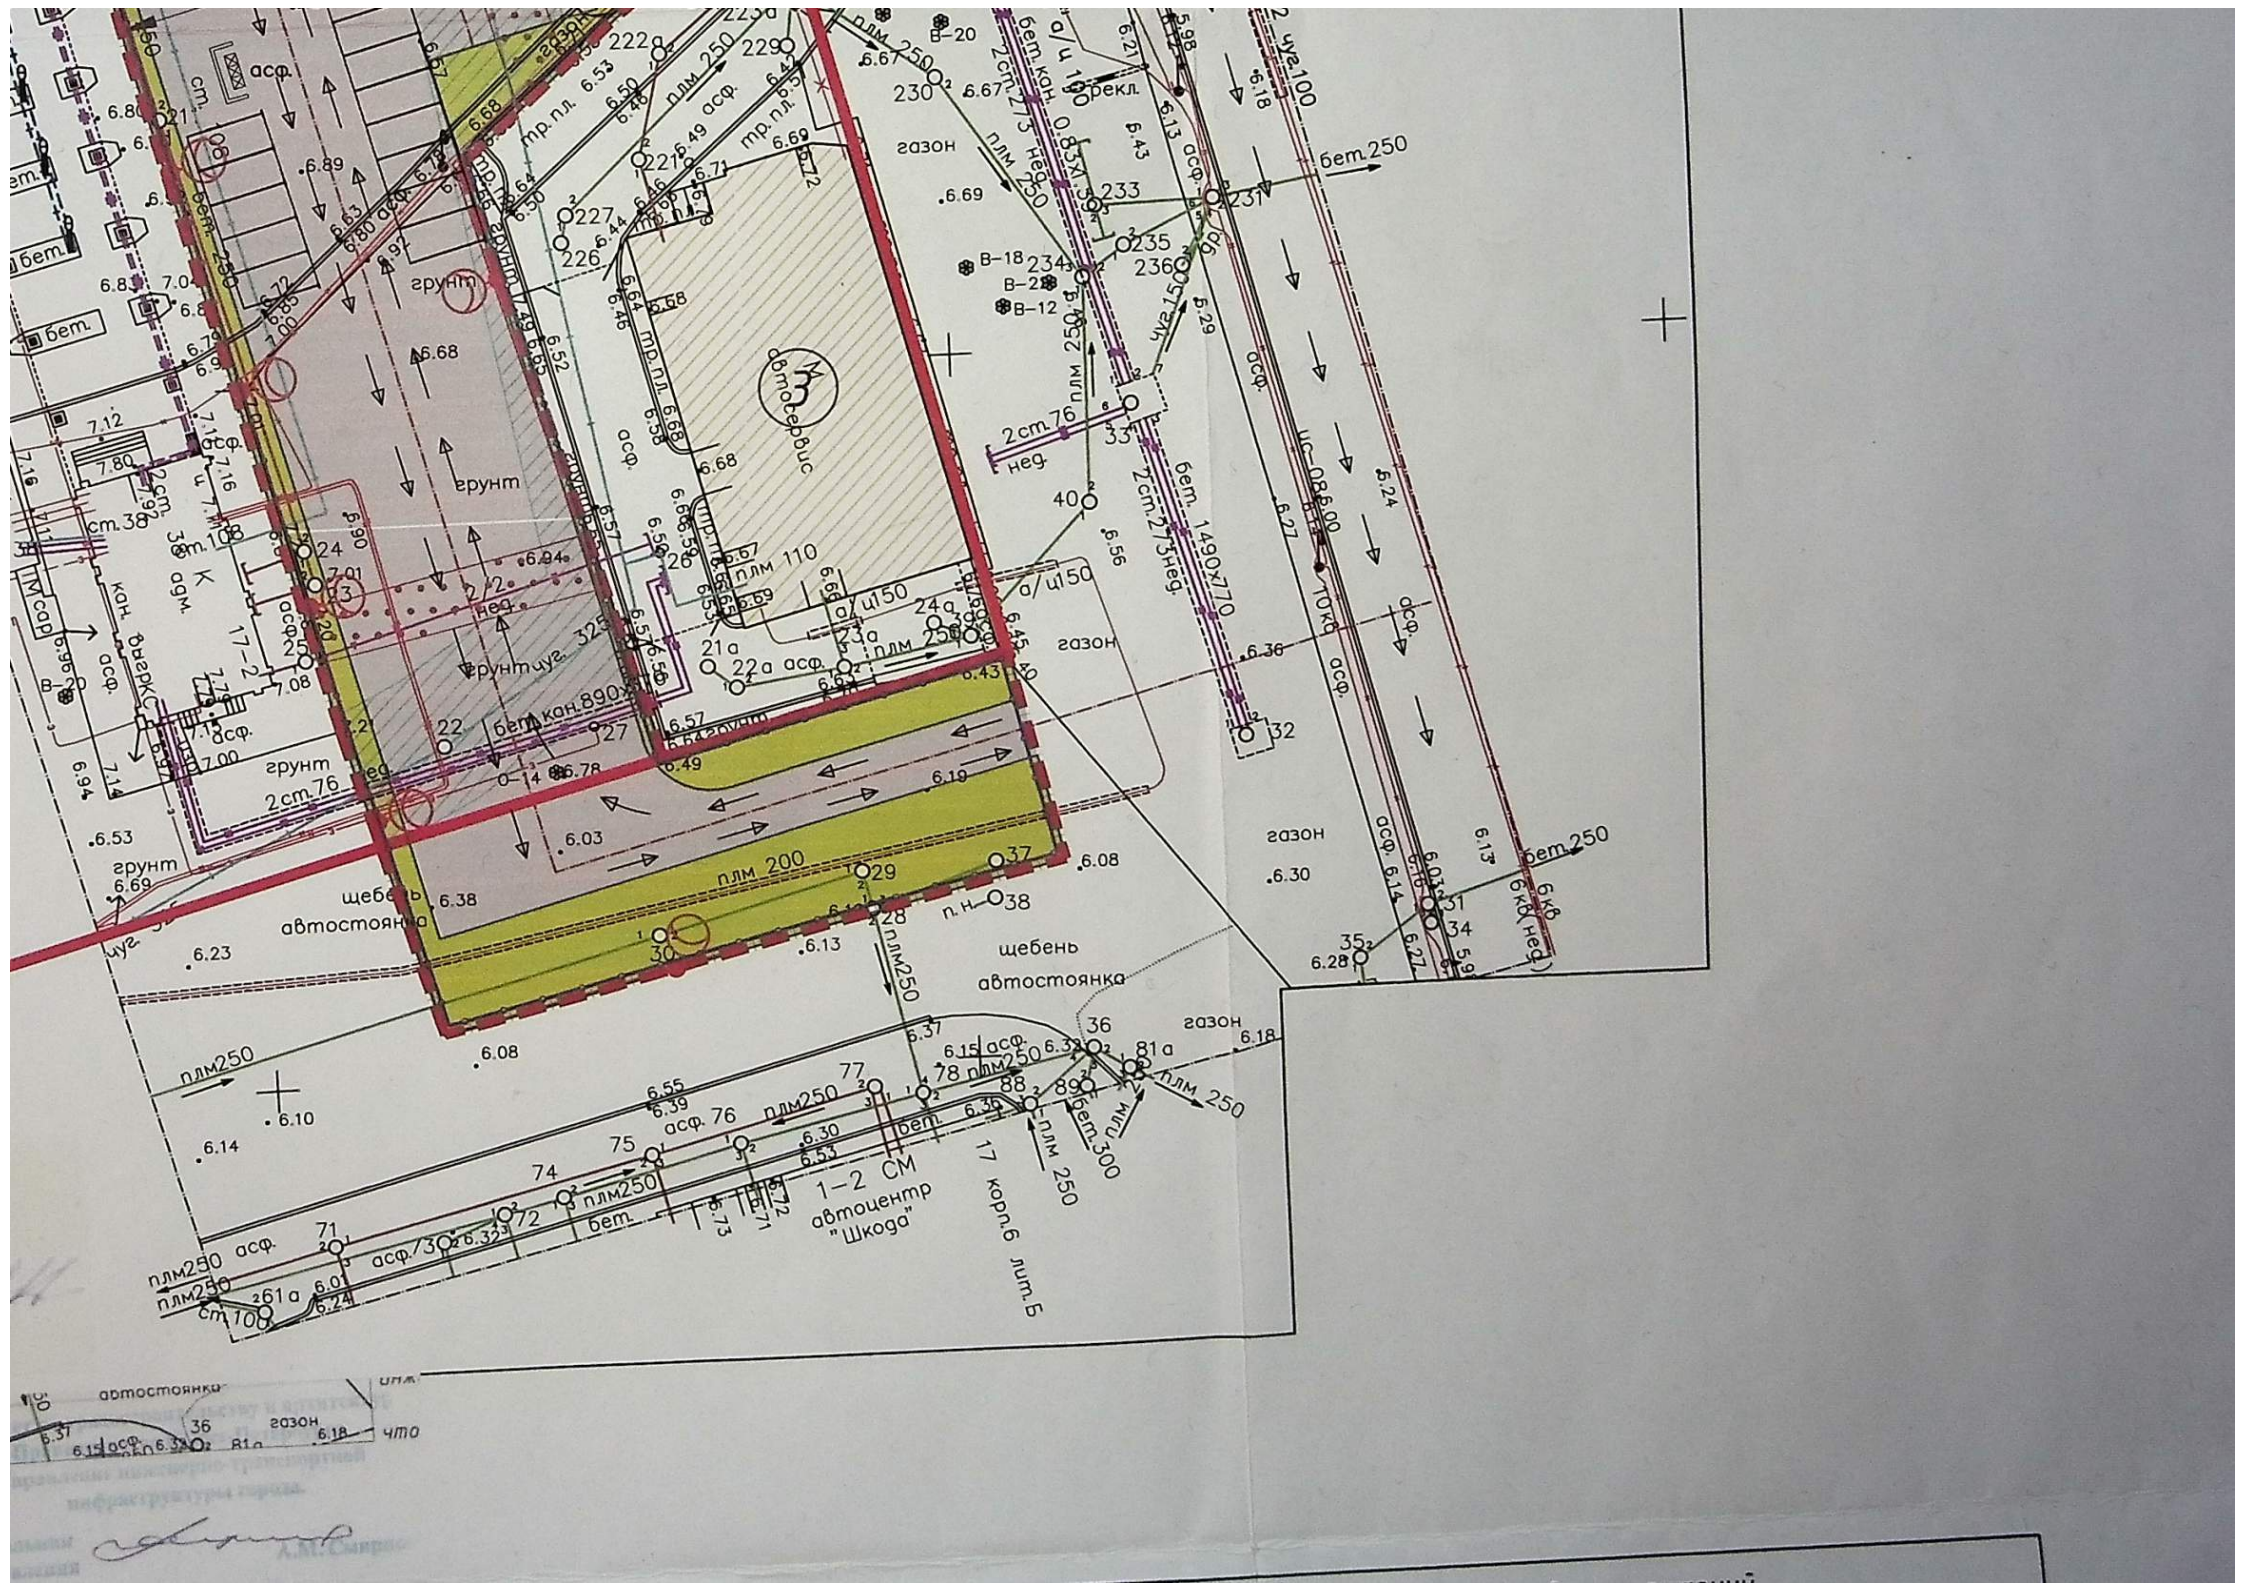
автосервис
3
грунт
газон
щебень
автостоянка
асф.
бет.
плм 250
плм 200
плм 110
1-2 СМ
автоцентр
"Шкода"
17 корп.6 лит.Б
1490х770
890х

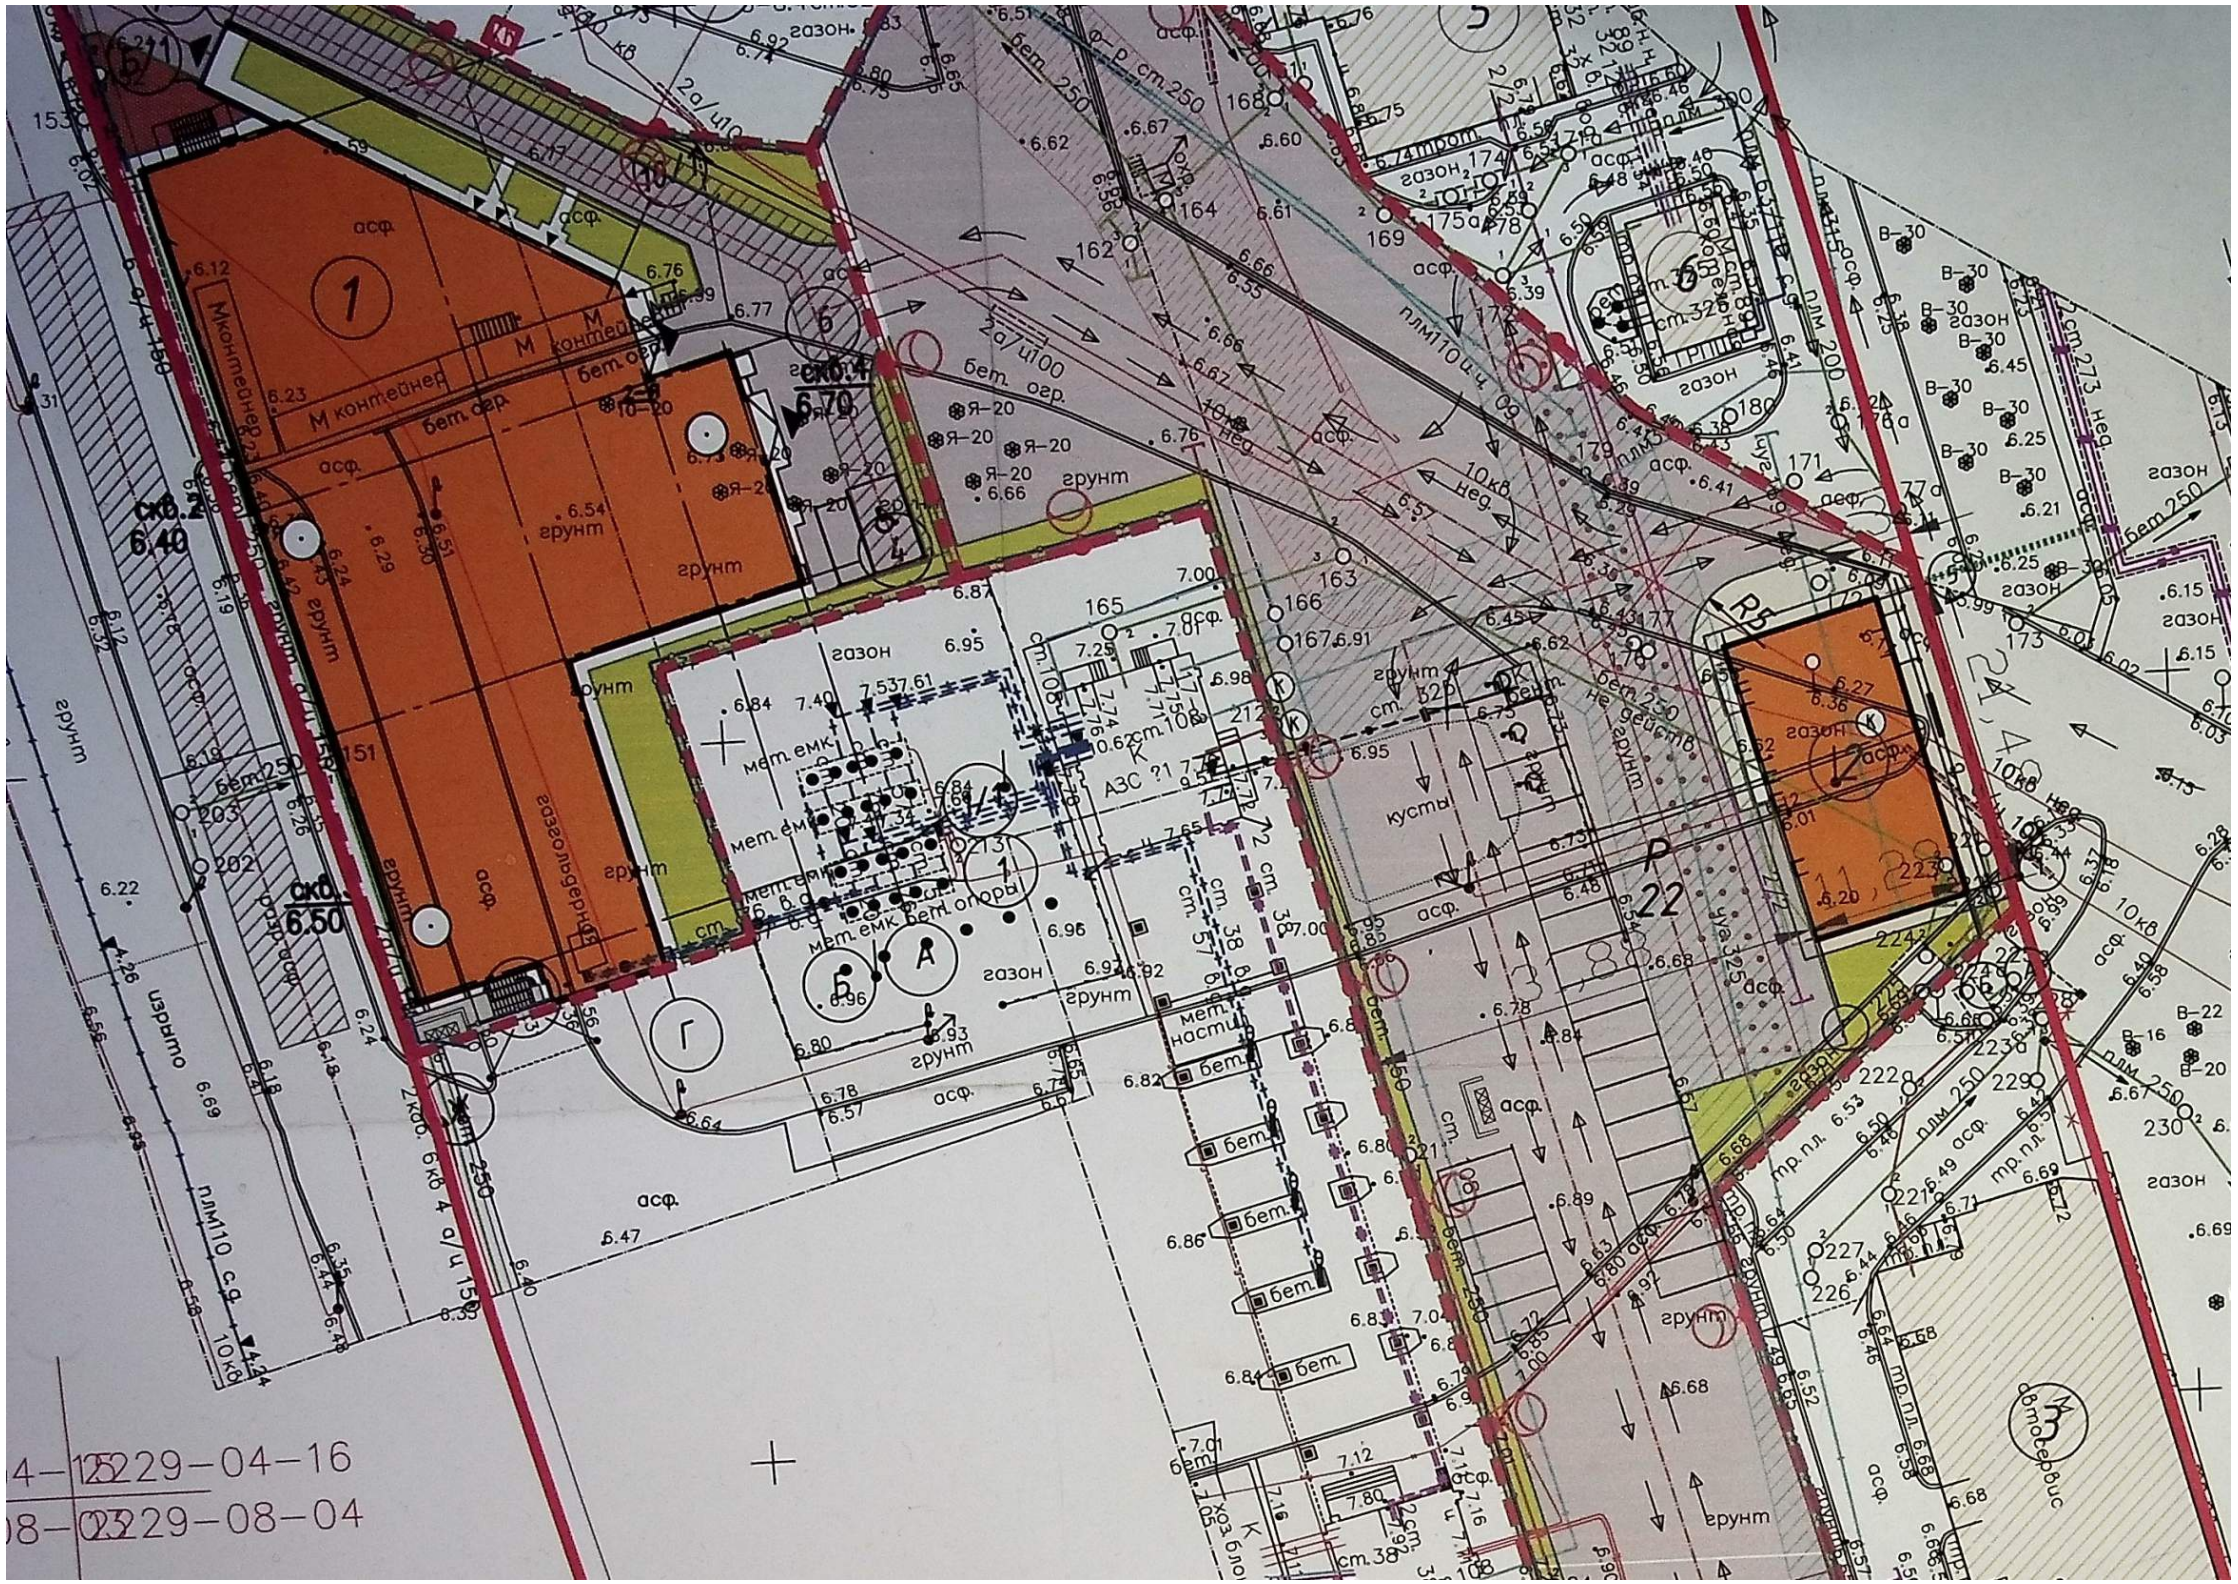
229-04-16
229-08-04
АЗС
Автосервис
М контейнер
бет. огр.
асф.
грунт
газон
мет. емк.
бет. опоры
кусты
газольдерная
хоз. блок
ск0.1
6.70
ск0.2
6.40
ск0.
6.50